


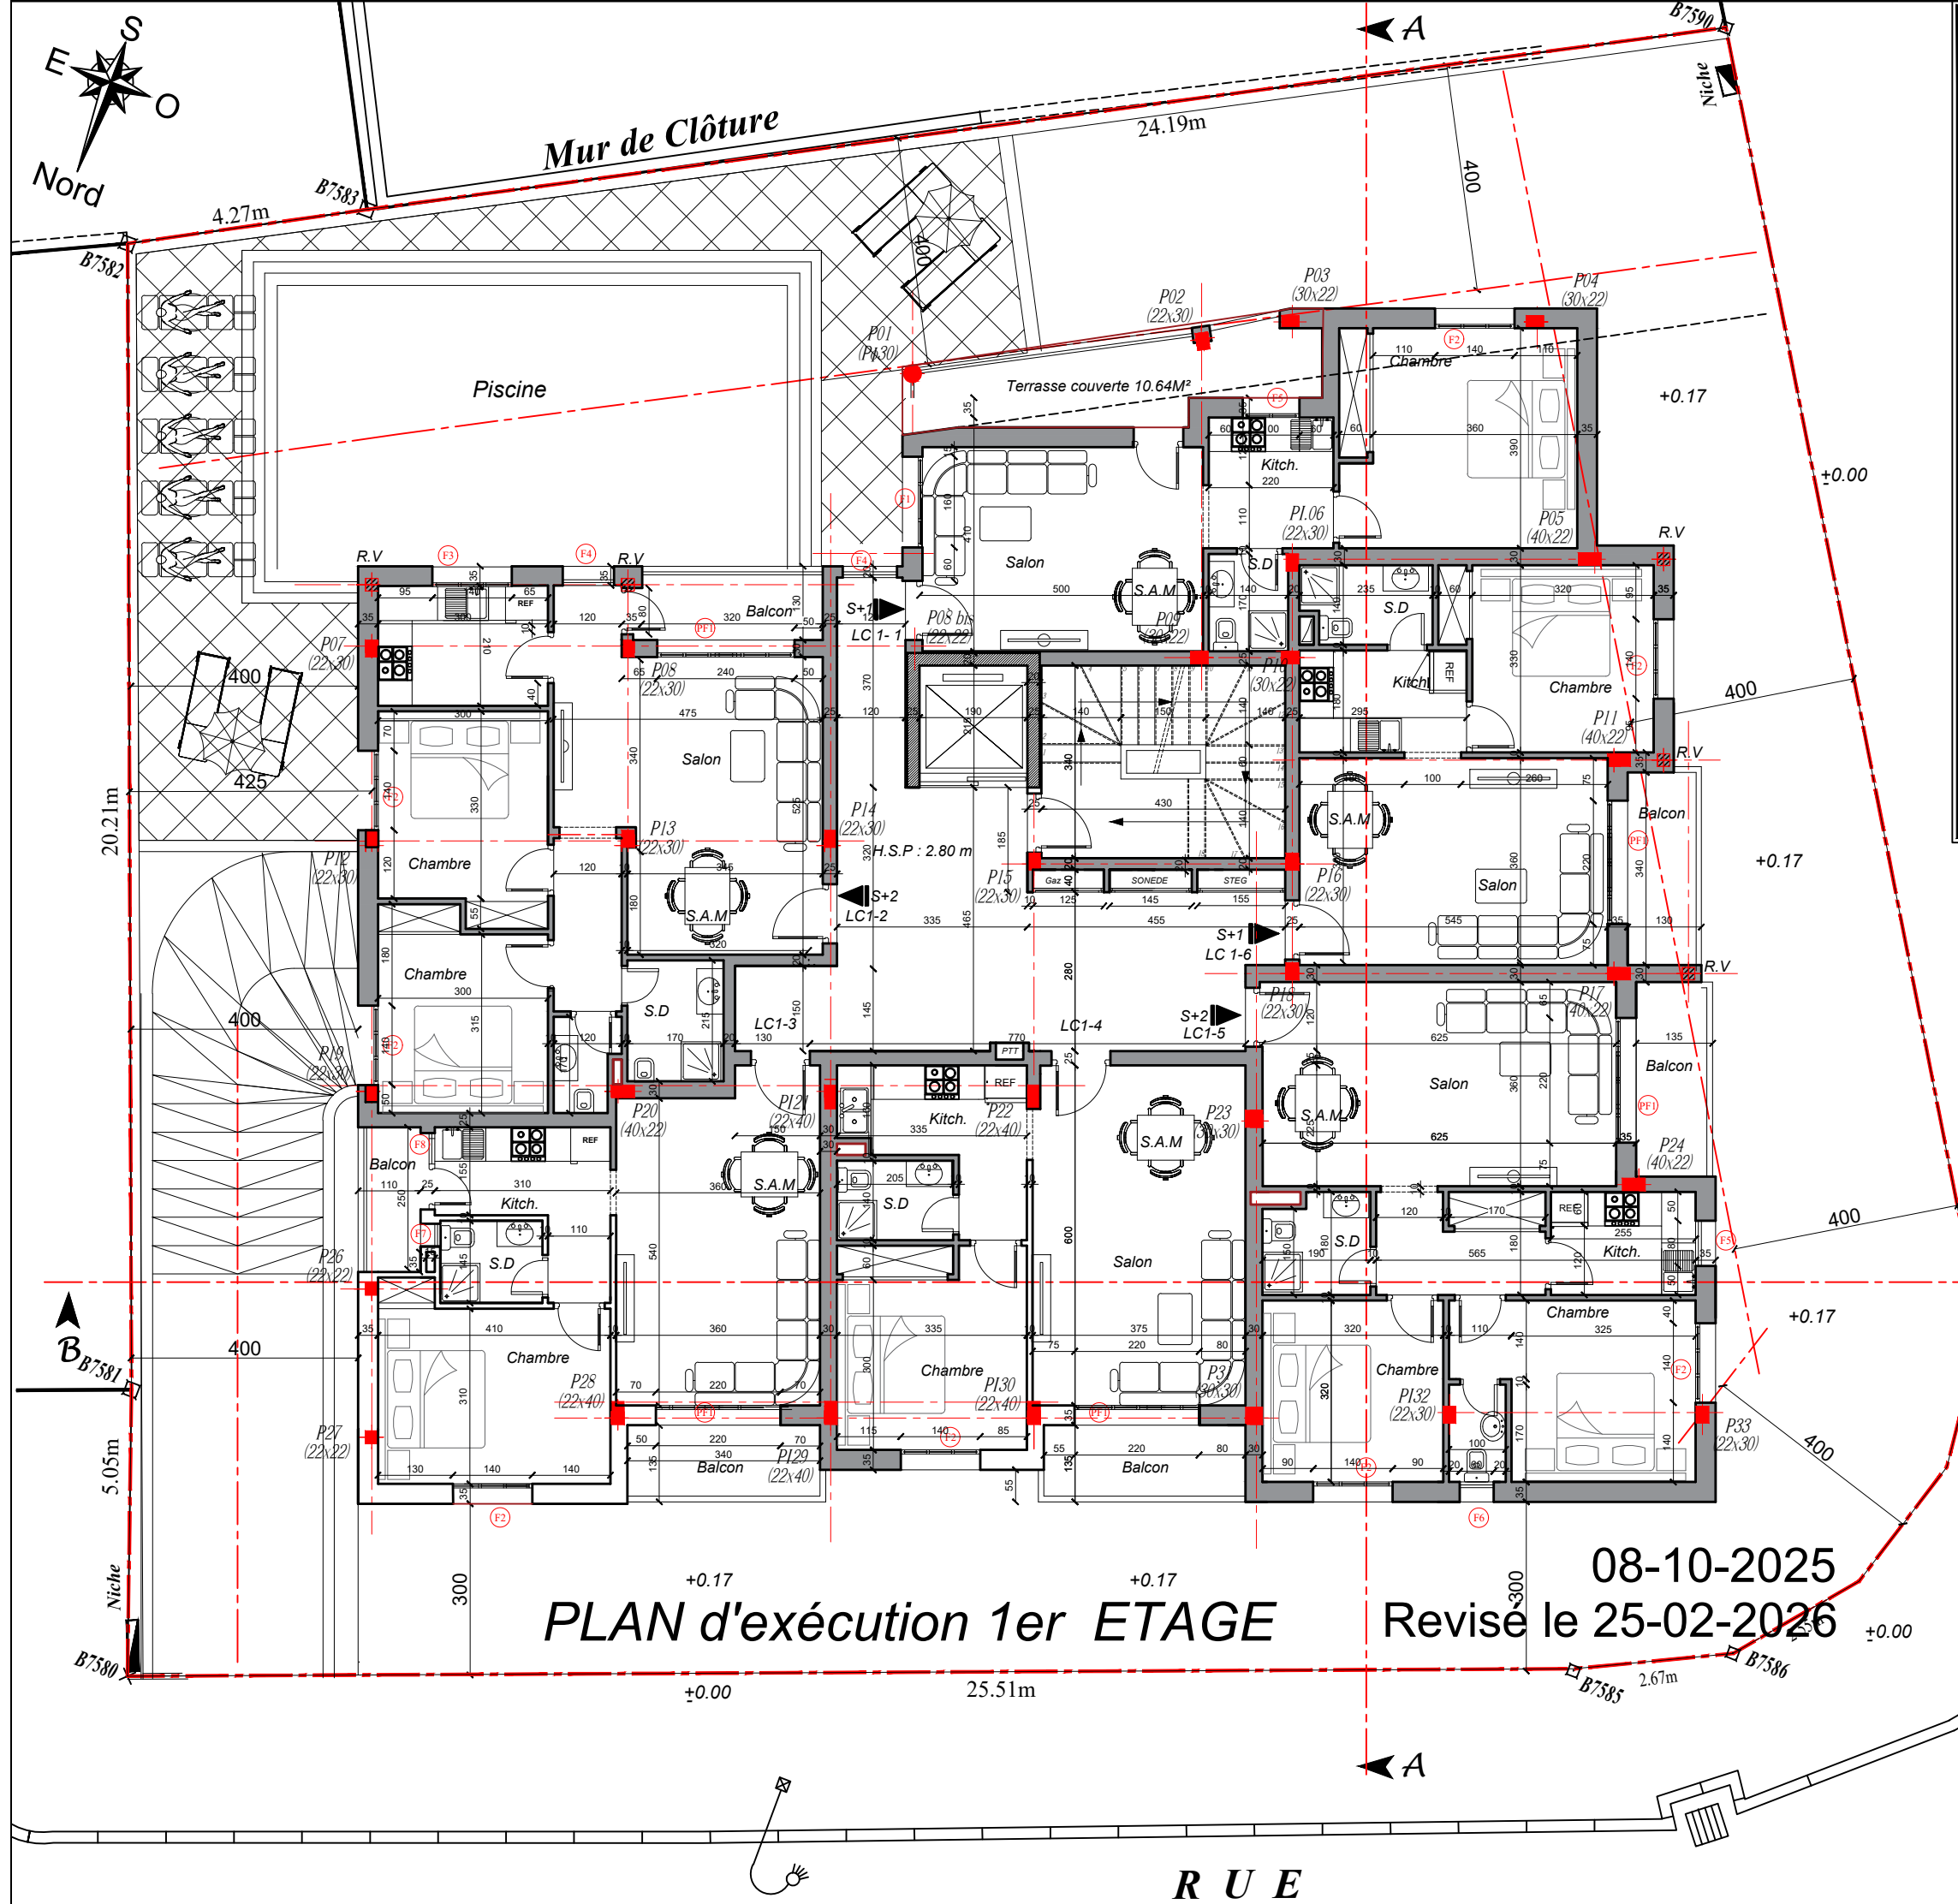

REPUBLIQUE TUNISIENNE
GOUVERNORAT DE NABEUL
COMMUNE DE NABEUL

COMPLEXE LES ORANGERS
CONSTRUCTION D UN IMMEUBLE Sous-sol + R+3
A USAGE COMMERCIAL
Lot E68 Sis à La Cité EL WAFIA LOTISSEMENT AFH
TITRE FONCIER : 664287 NABEUL

Propriétaire : Mme NADIA BOUSSEMA BRAHAM

DOSSIER
PERMIS DE BATIR

DESIGNATION :

PLAN 1er ETAGE

PLANCHE :1/-/-/- ECH 1/50 Oct 2024

VISA OAT
N° 795066656

INTITULE DU PROJET
immeuble a usage commercial
NUMERO DU TITRE/LOT/PARCELLE
#68
SURFACE DU TERRAIN
836 m²
MAITRE D'OUVRAGE
Nadia boussema braham
SURF. TOTALE COUVERTE APPROXIMATIVE
750 m²
Modèle enregistré à l'INRORP1 - Toute reproduction interdite
Visa OAT pour permis de bâtir
Toute falsification conduit à des poursuites judiciaires

A848455100300
Nabeul, le: 18/11/2020

ARCHITECTE
SGHAIER Mohamed

ADRESSE
8, Rue de Kairouan

TELEPHONE 71841257 FAX 71846302
GSM 22320075
E-MAIL bureausghaier@gmail.com
MATRICULE FISCAL 91811HIA/P1000